


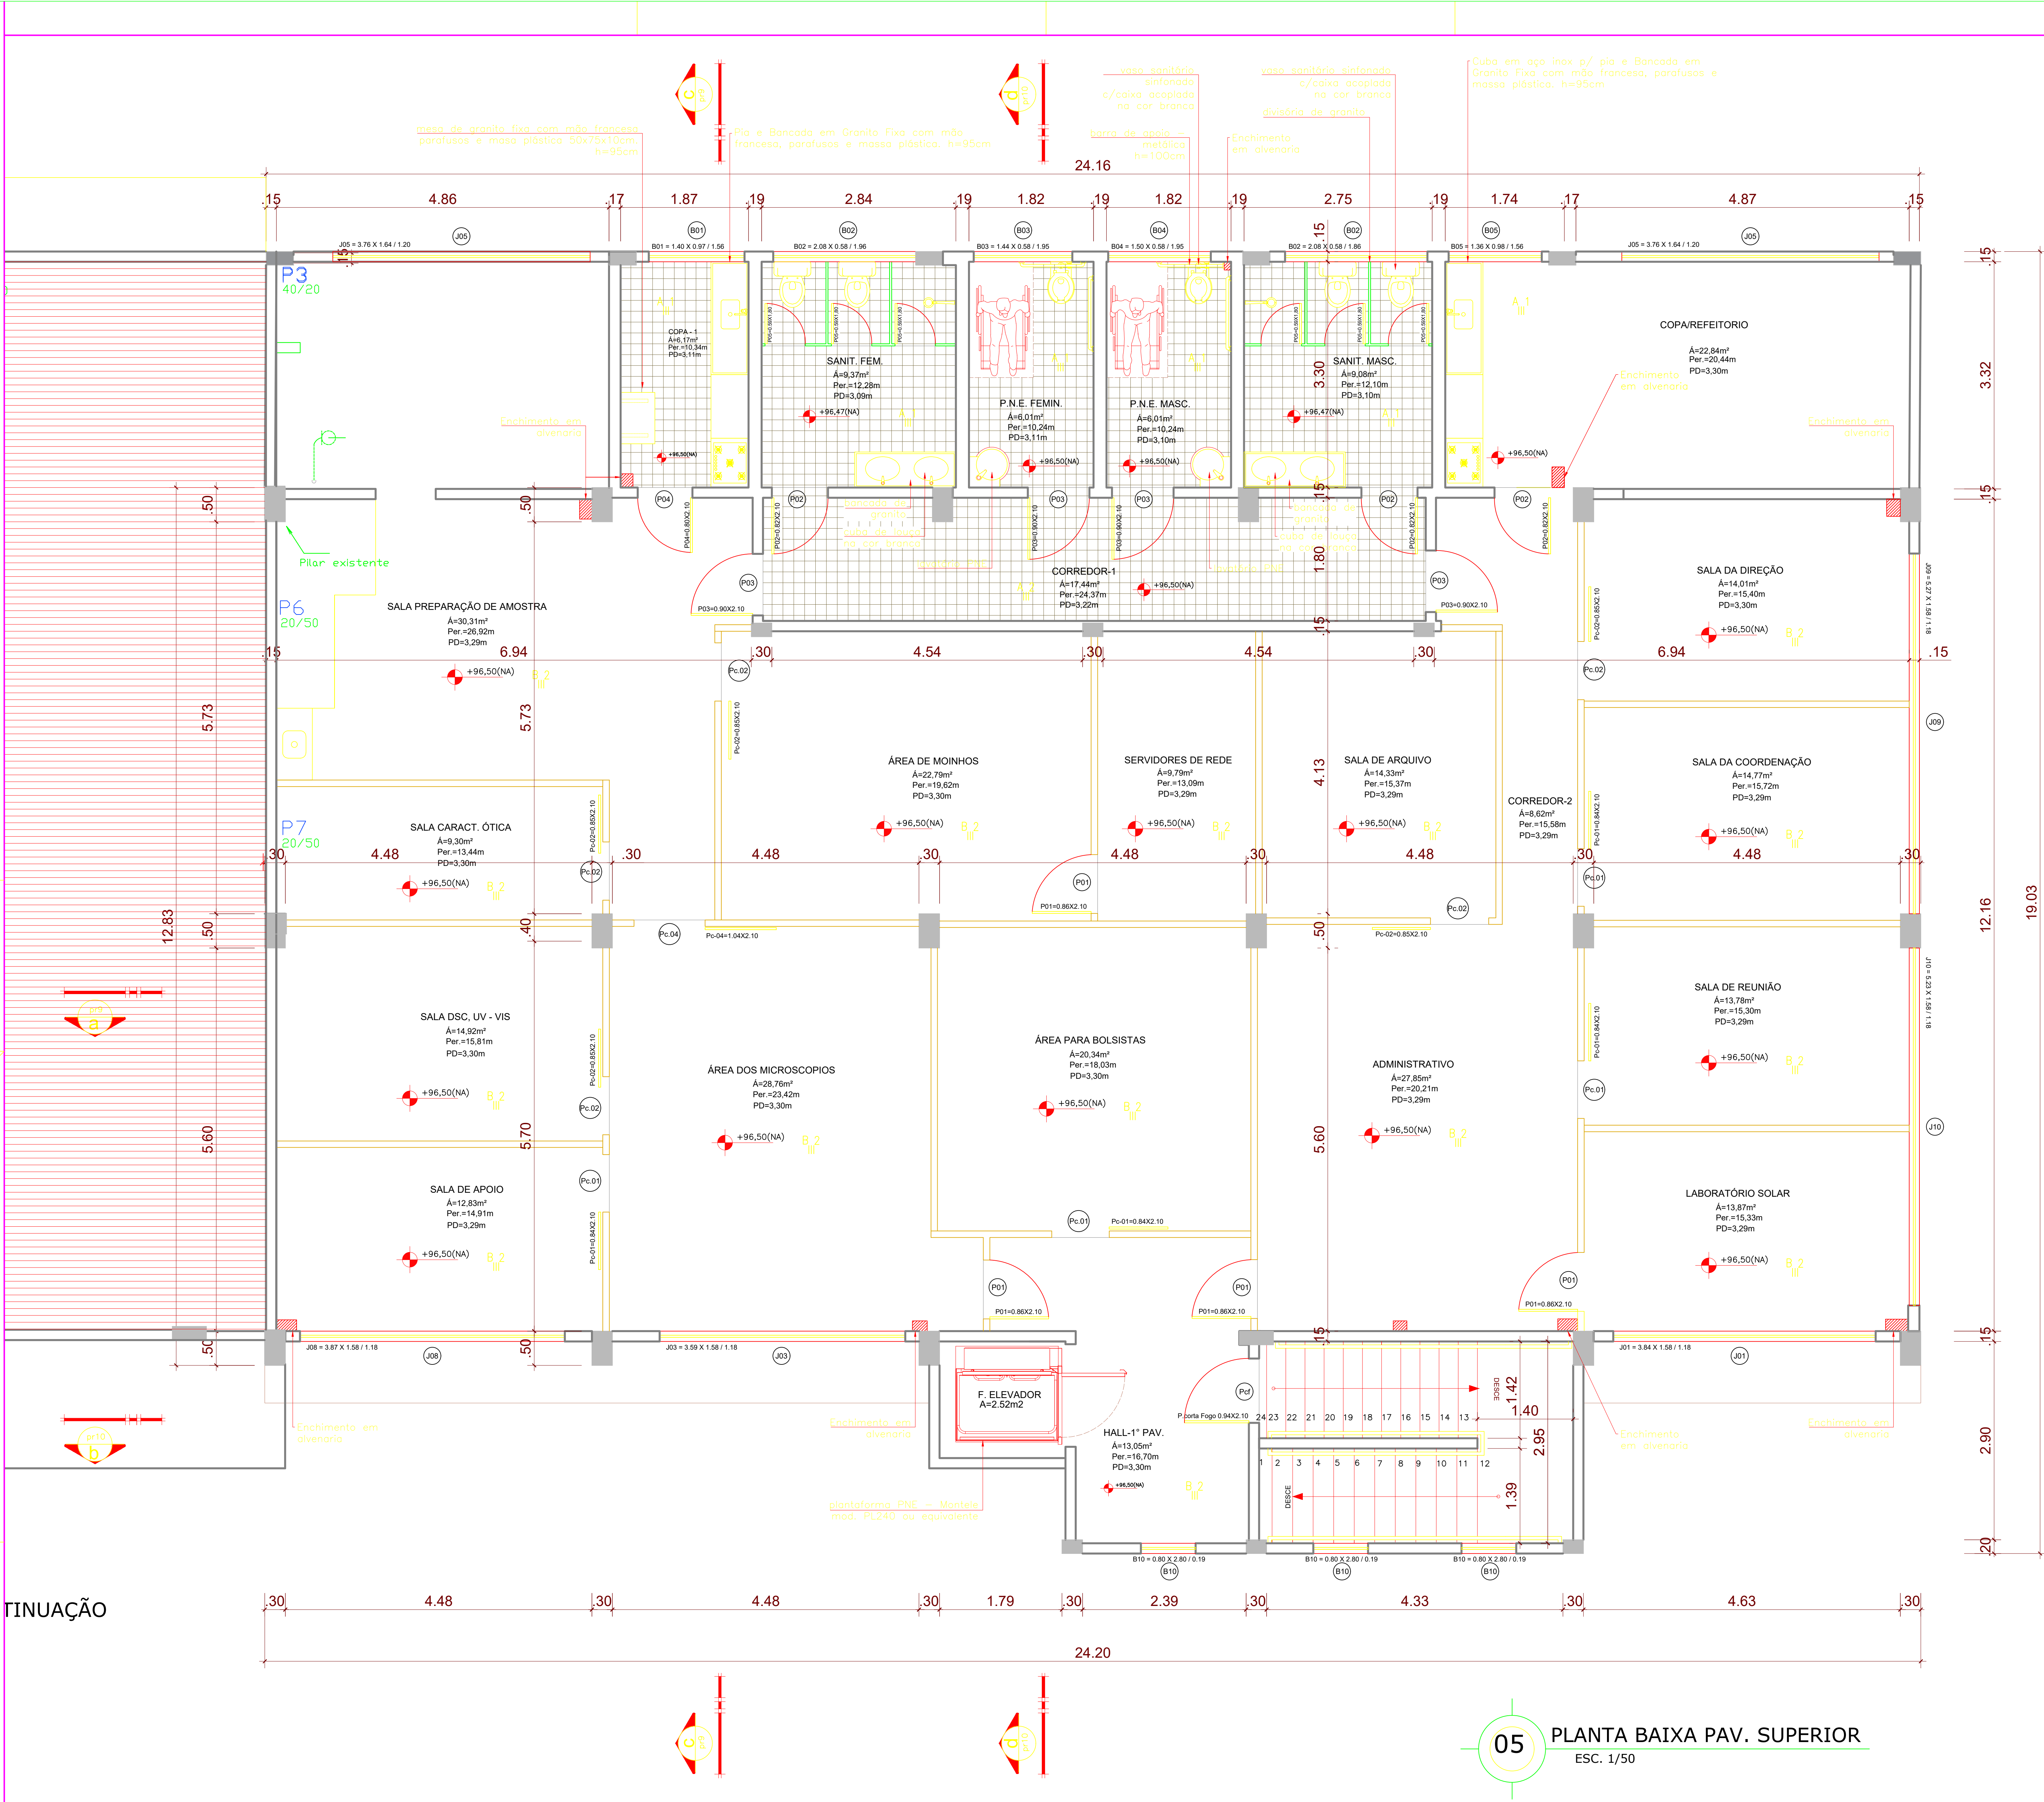

05 PLANTA BAIXA PAV. SUPERIOR
ESC. 1/50

REVISÃO:	DESCRIÇÃO:	DATA:	TABELA ESQUADRIAS/ESPECIFICAÇÕES (TOTAL DA PRANCHA)						QUADRO DE ÁREAS	REGISTRO CONTROLE INTERNO	LEGENDA:
REV00		DEZEMBRO DE 2012							ÁREA DO TERRENO:	CARTÓRIO:	PRD
REV01	Conforme parecer técnico 05/2013	MAIO DE 2013							ÁREA PAVIMENTO TERREO:	X CARTÓRIO	AL REVESTIMENTO
									ÁREA PAVIMENTO SUPERIOR:	DESENHO:	AL REVESTIMENTO
									ÁREA CONSTRUÇÃO TOTAL:	NOME: ANO: LIVRO:	AL REVESTIMENTO
										CARIMBOMATRIZ-REV01	AL REVESTIMENTO
										CARIMBOMATRIZ-REV01	AL REVESTIMENTO

MODIFICAÇÕES NA FASE DE EXECUÇÃO DO PROJETO:									
- TODAS AS MEDIDAS DO PROJETO DE ARQUITETURA FORAM ATUALIZADAS CONFORME O EXECUTADO									
- FÔRRO - EM TODOS OS AMBIENTES QUE ESTAVA DESCRITO EM PROJETO "FÔRRO DE GESSO COM PINTURA LATEX, MUDOU PARA FÔRRO DE PVC COM RODA FORRO.									
- A ESCADA FOI EXECUTADA SEM A SINALIZAÇÃO TÁTIL NO PISO, COMO ESTAR EM PROJETO EXECUTIVO DE ARQUITETURA (ARQ.CMDI_MANAUAS DISTRITO(Pr. 04a19).R1.dwg) 04/19									
- A PASSARELA DE ENTRADA FOI EXECUTADA SEM A SINALIZAÇÃO NO PISO TÁTIL, COMO ESTAR EM PROJETO EXECUTIVO DE ARQUITETURA (ARQ.CMDI_MANAUAS DISTRITO(Pr. 04a19).R1.dwg) 04/19									
- OS PILARES; P14, P15, P16, P17, P18, P19, MUDARAM DE SEÇÃO DE (30X30 cm), PARA (50 X 30 cm).									